


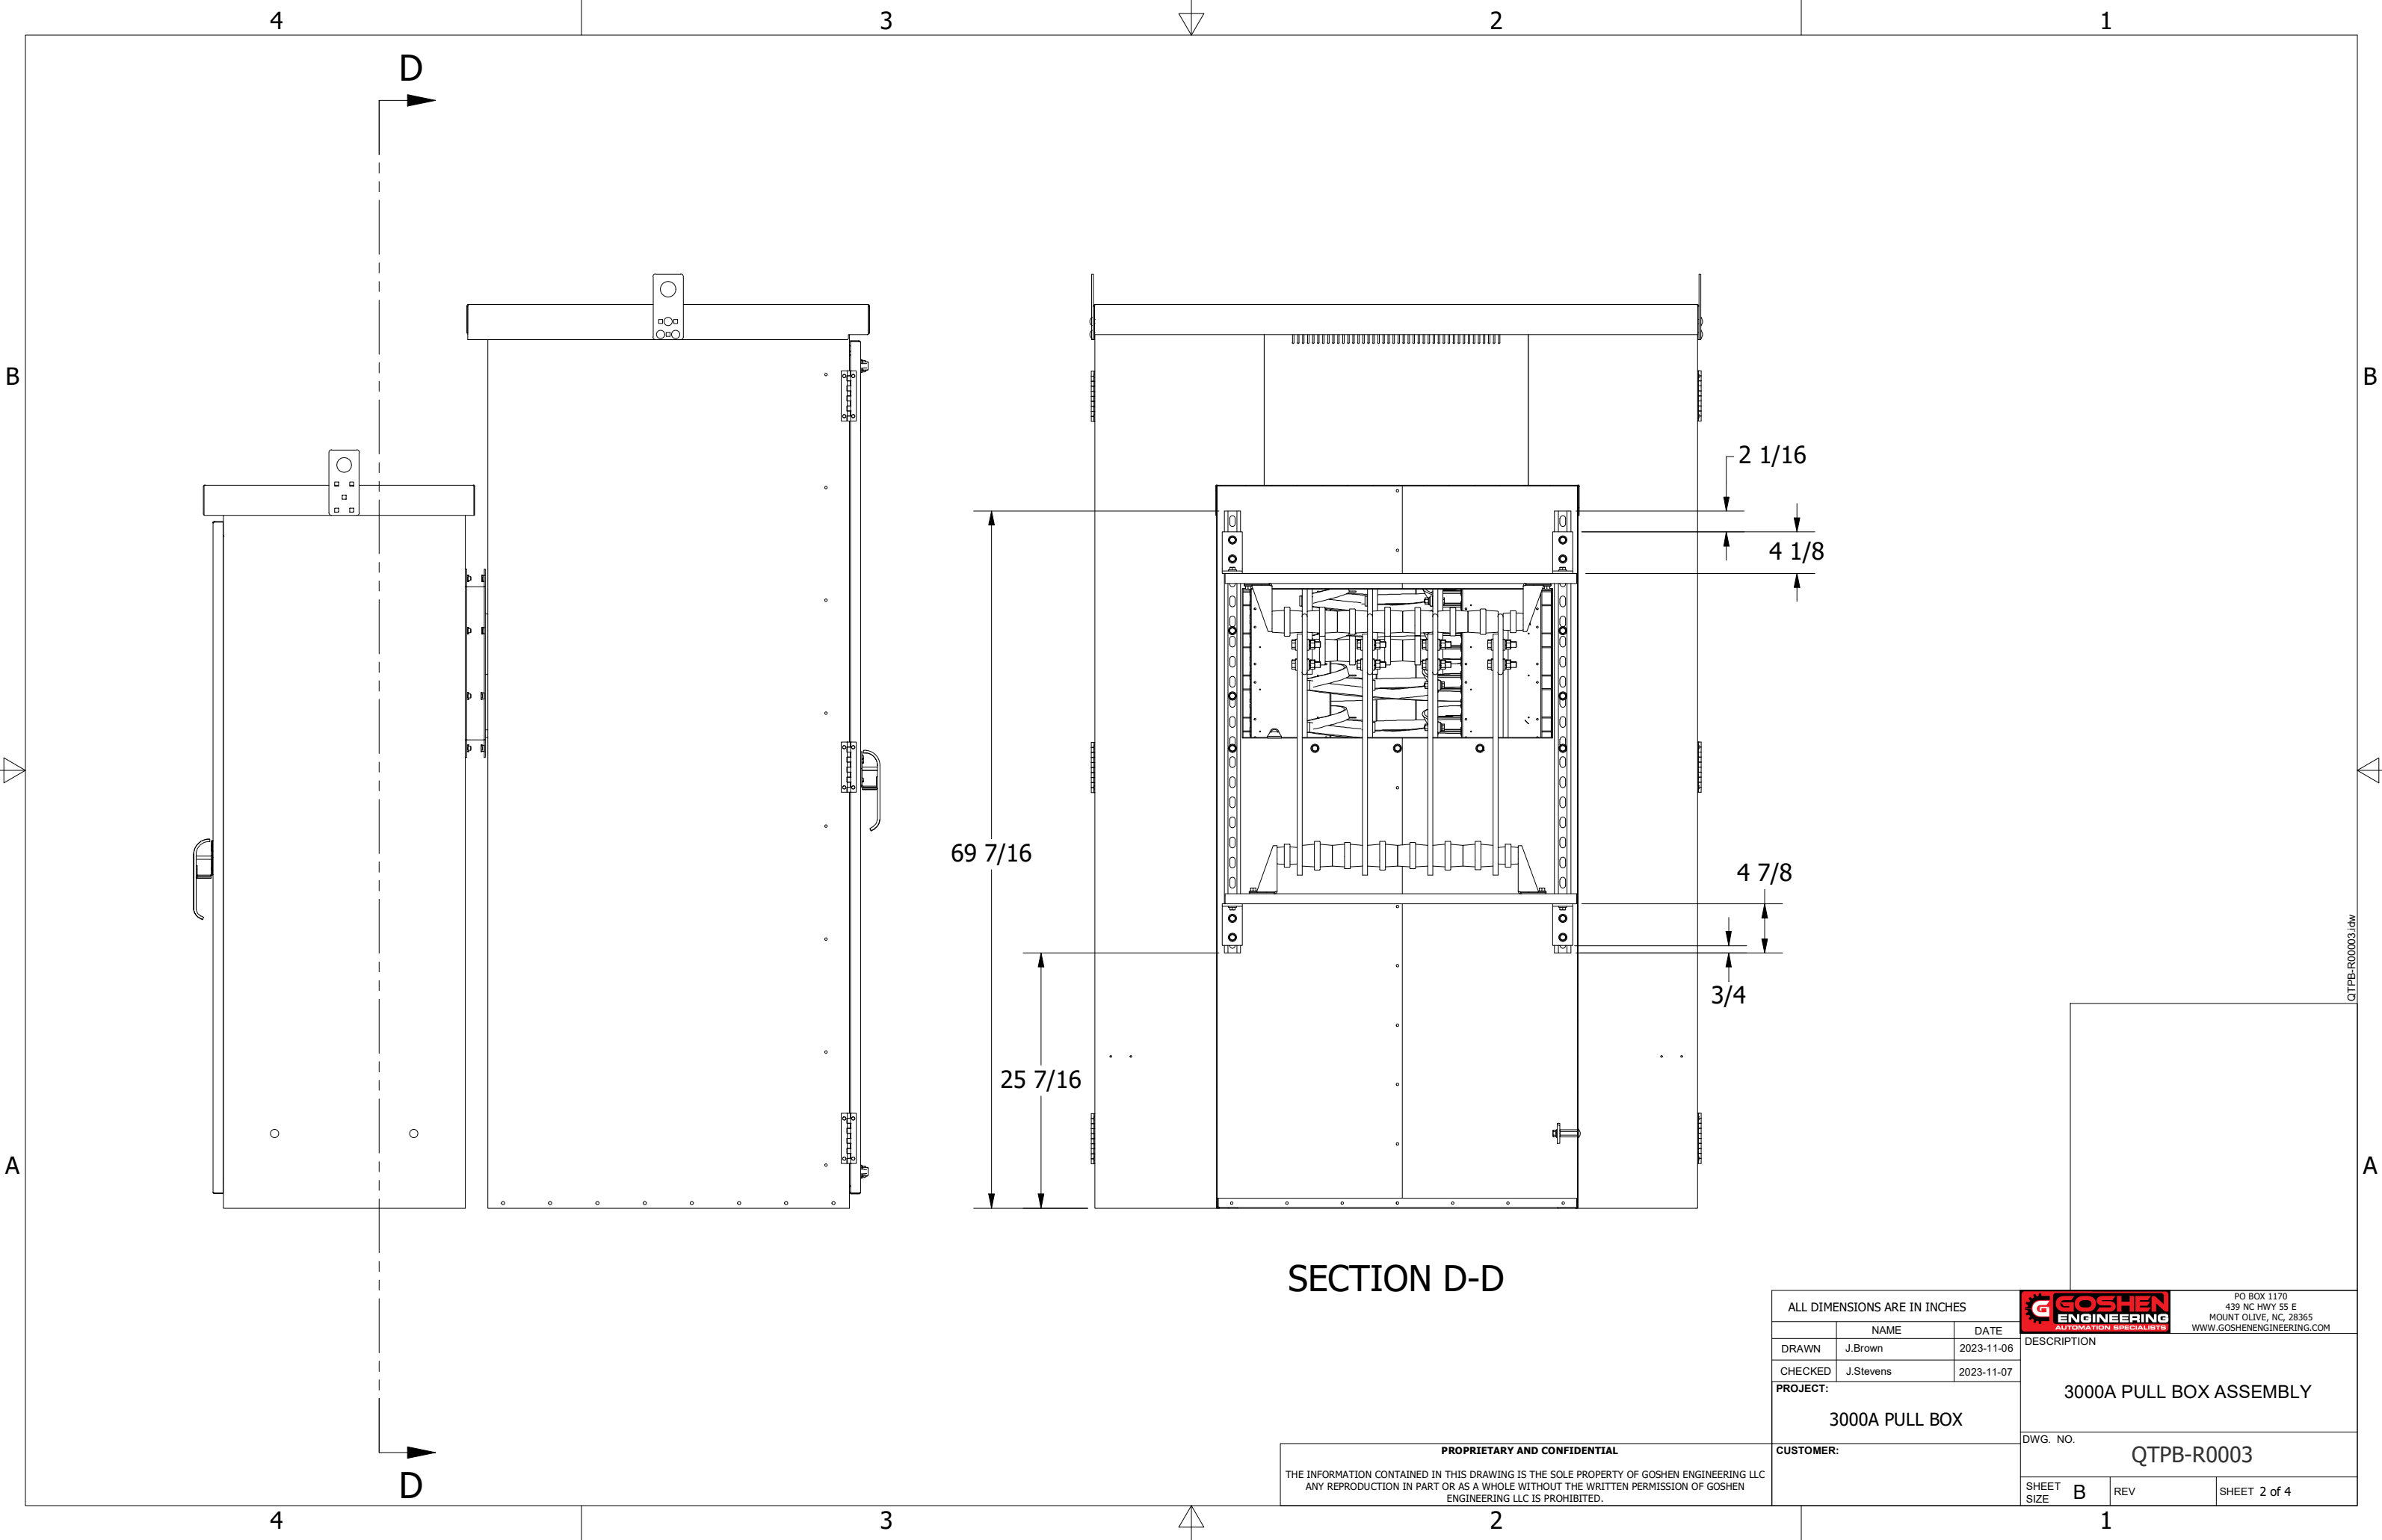

SECTION D-D

ALL DIMENSIONS ARE IN INCHES			 PO BOX 1170 439 NC HWY 55 E MOUNT OLIVE, NC, 28365 WWW.GOSHENENGINEERING.COM	
	NAME	DATE		DESCRIPTION
DRAWN	J.Brown	2023-11-06		
CHECKED	J.Stevens	2023-11-07		
PROJECT: 3000A PULL BOX			3000A PULL BOX ASSEMBLY	
CUSTOMER:			DWG. NO. QTPB-R0003	
			SHEET SIZE B	
			REV	
			SHEET 2 of 4	

4

3


2

1

NOTES:

- 1. USE 1" SET SCREW (ITEM 15) WHEN STACKING TWO INSULATORS.
- 2. USE 1.5" SET SCREW (ITEM 16) WHEN COPPER BUS IS STACKED BETWEEN TWO INSULATORS.
- 3. TORQUE 3/8" HEX HEAD BOLTS TO 26 ft-lb.
- 4. TORQUE 1/2" HEX HEAD BOLTS TO 64 ft-lb.


B

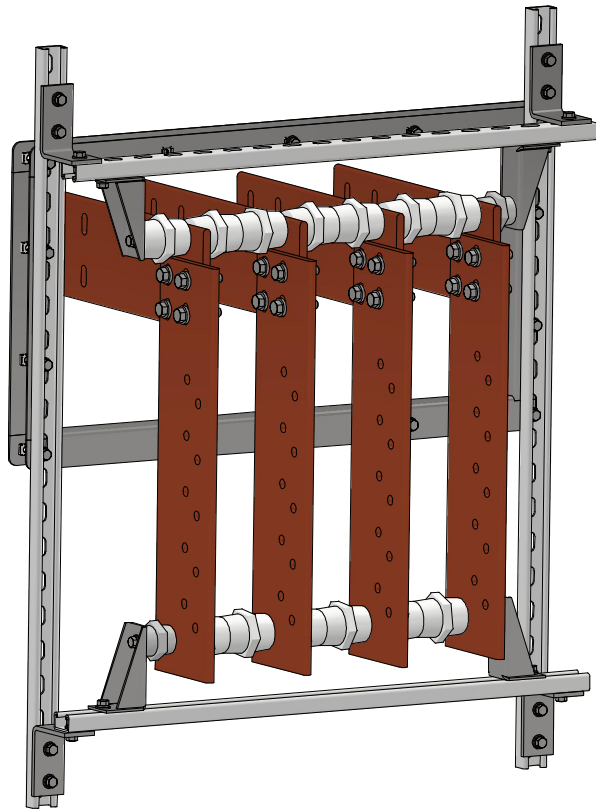

26 23 24 25

DETAIL A

A

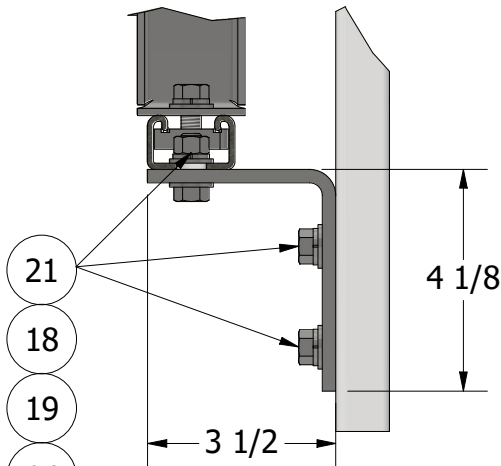


DETAIL B

4

3


2

1

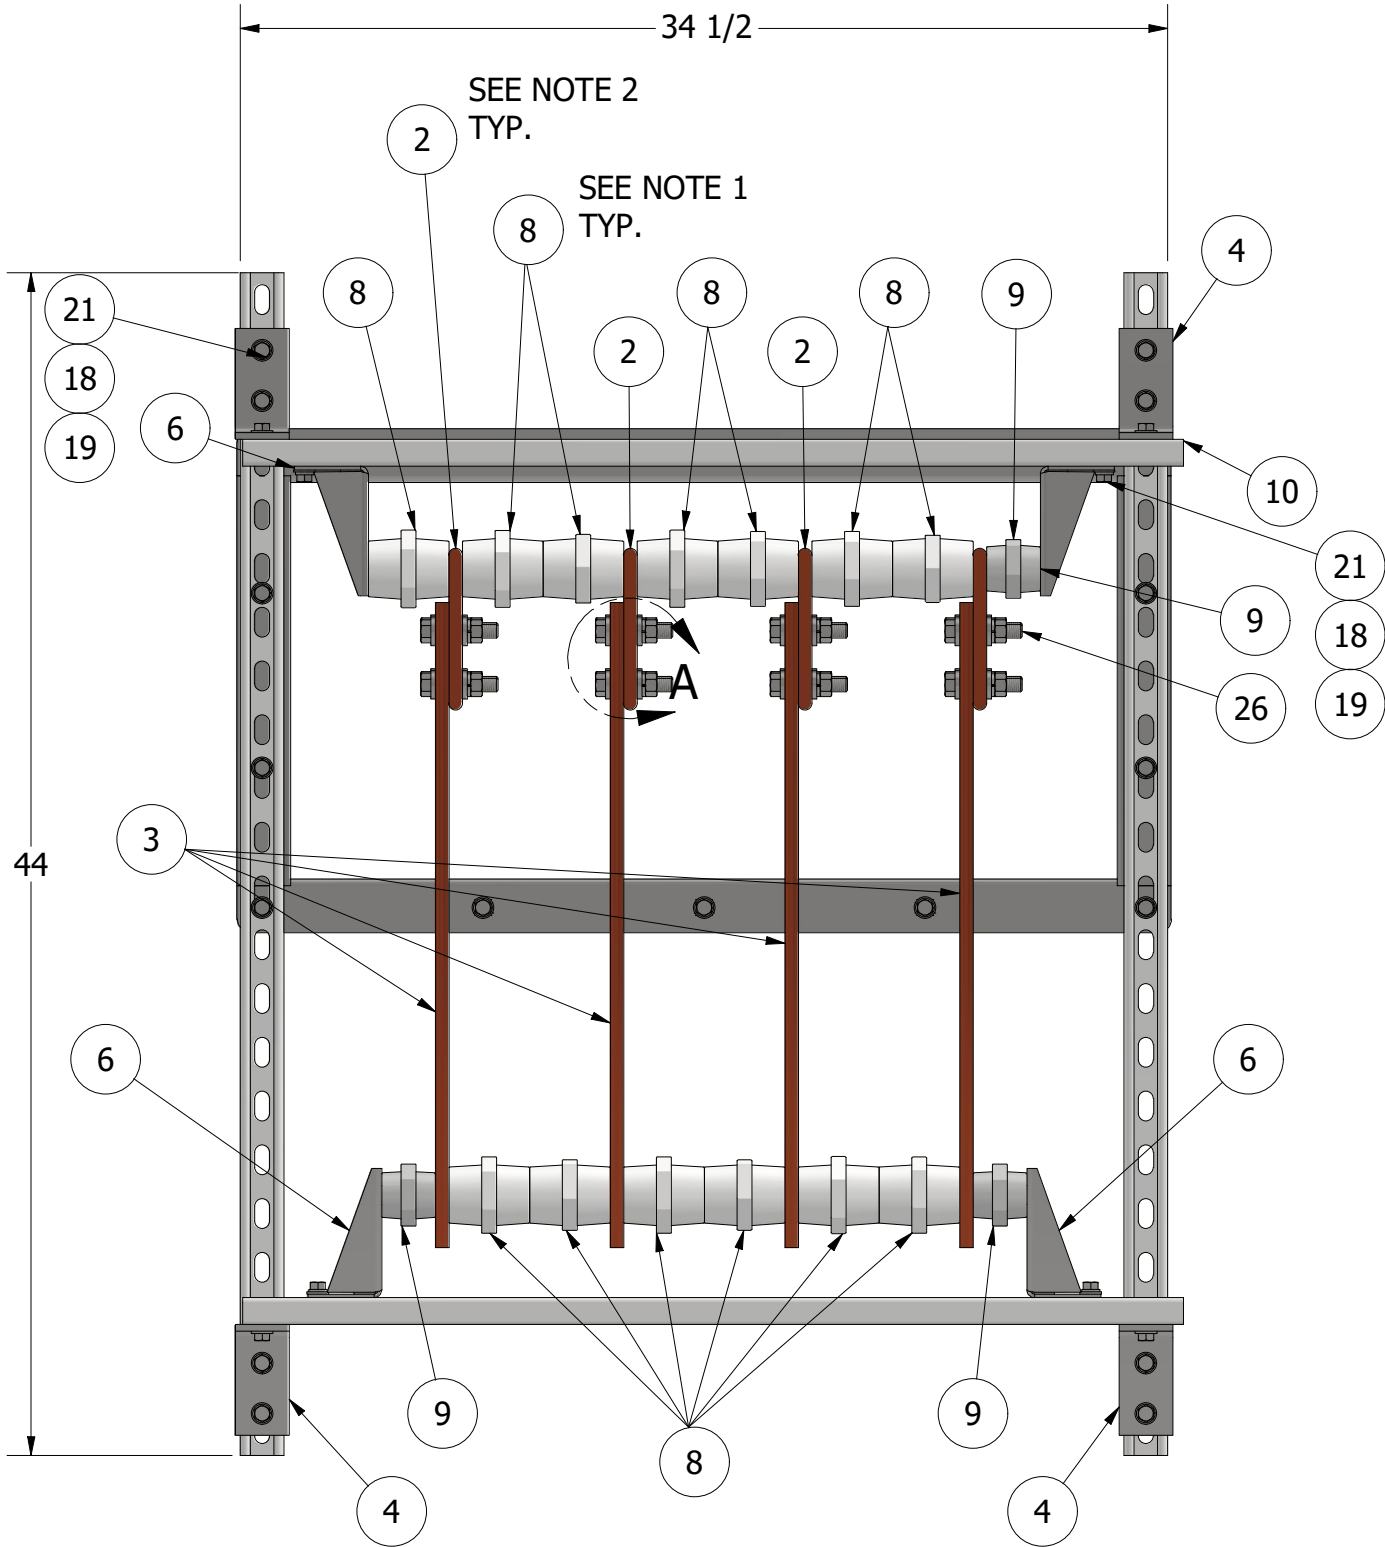


B

A

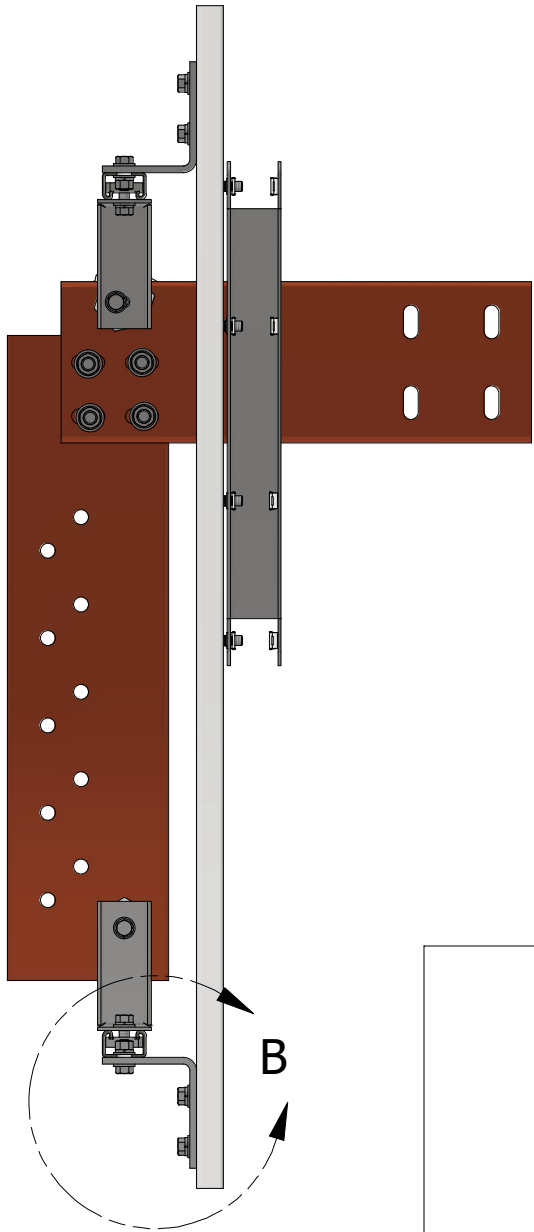

PROPRIETARY AND CONFIDENTIAL
THE INFORMATION CONTAINED IN THIS DRAWING IS THE SOLE PROPERTY OF GOSHEN ENGINEERING LLC
ANY REPRODUCTION IN PART OR AS A WHOLE WITHOUT THE WRITTEN PERMISSION OF GOSHEN
ENGINEERING LLC IS PROHIBITED.

ALL DIMENSIONS ARE IN INCHES			 PO BOX 1170 439 NC HWY 55 E MOUNT OLIVE, NC, 28365 WWW.GOSHENENGINEERING.COM	
	NAME	DATE		DESCRIPTION
DRAWN	J.Brown	2023-11-06		
CHECKED	J.Stevens	2023-11-07		
PROJECT: 3000A PULL BOX			3000A PULL BOX ASSEMBLY	
CUSTOMER:			DWG. NO. QTPB-R0003	
SHEET SIZE	B	REV	SHEET 3 of 4	

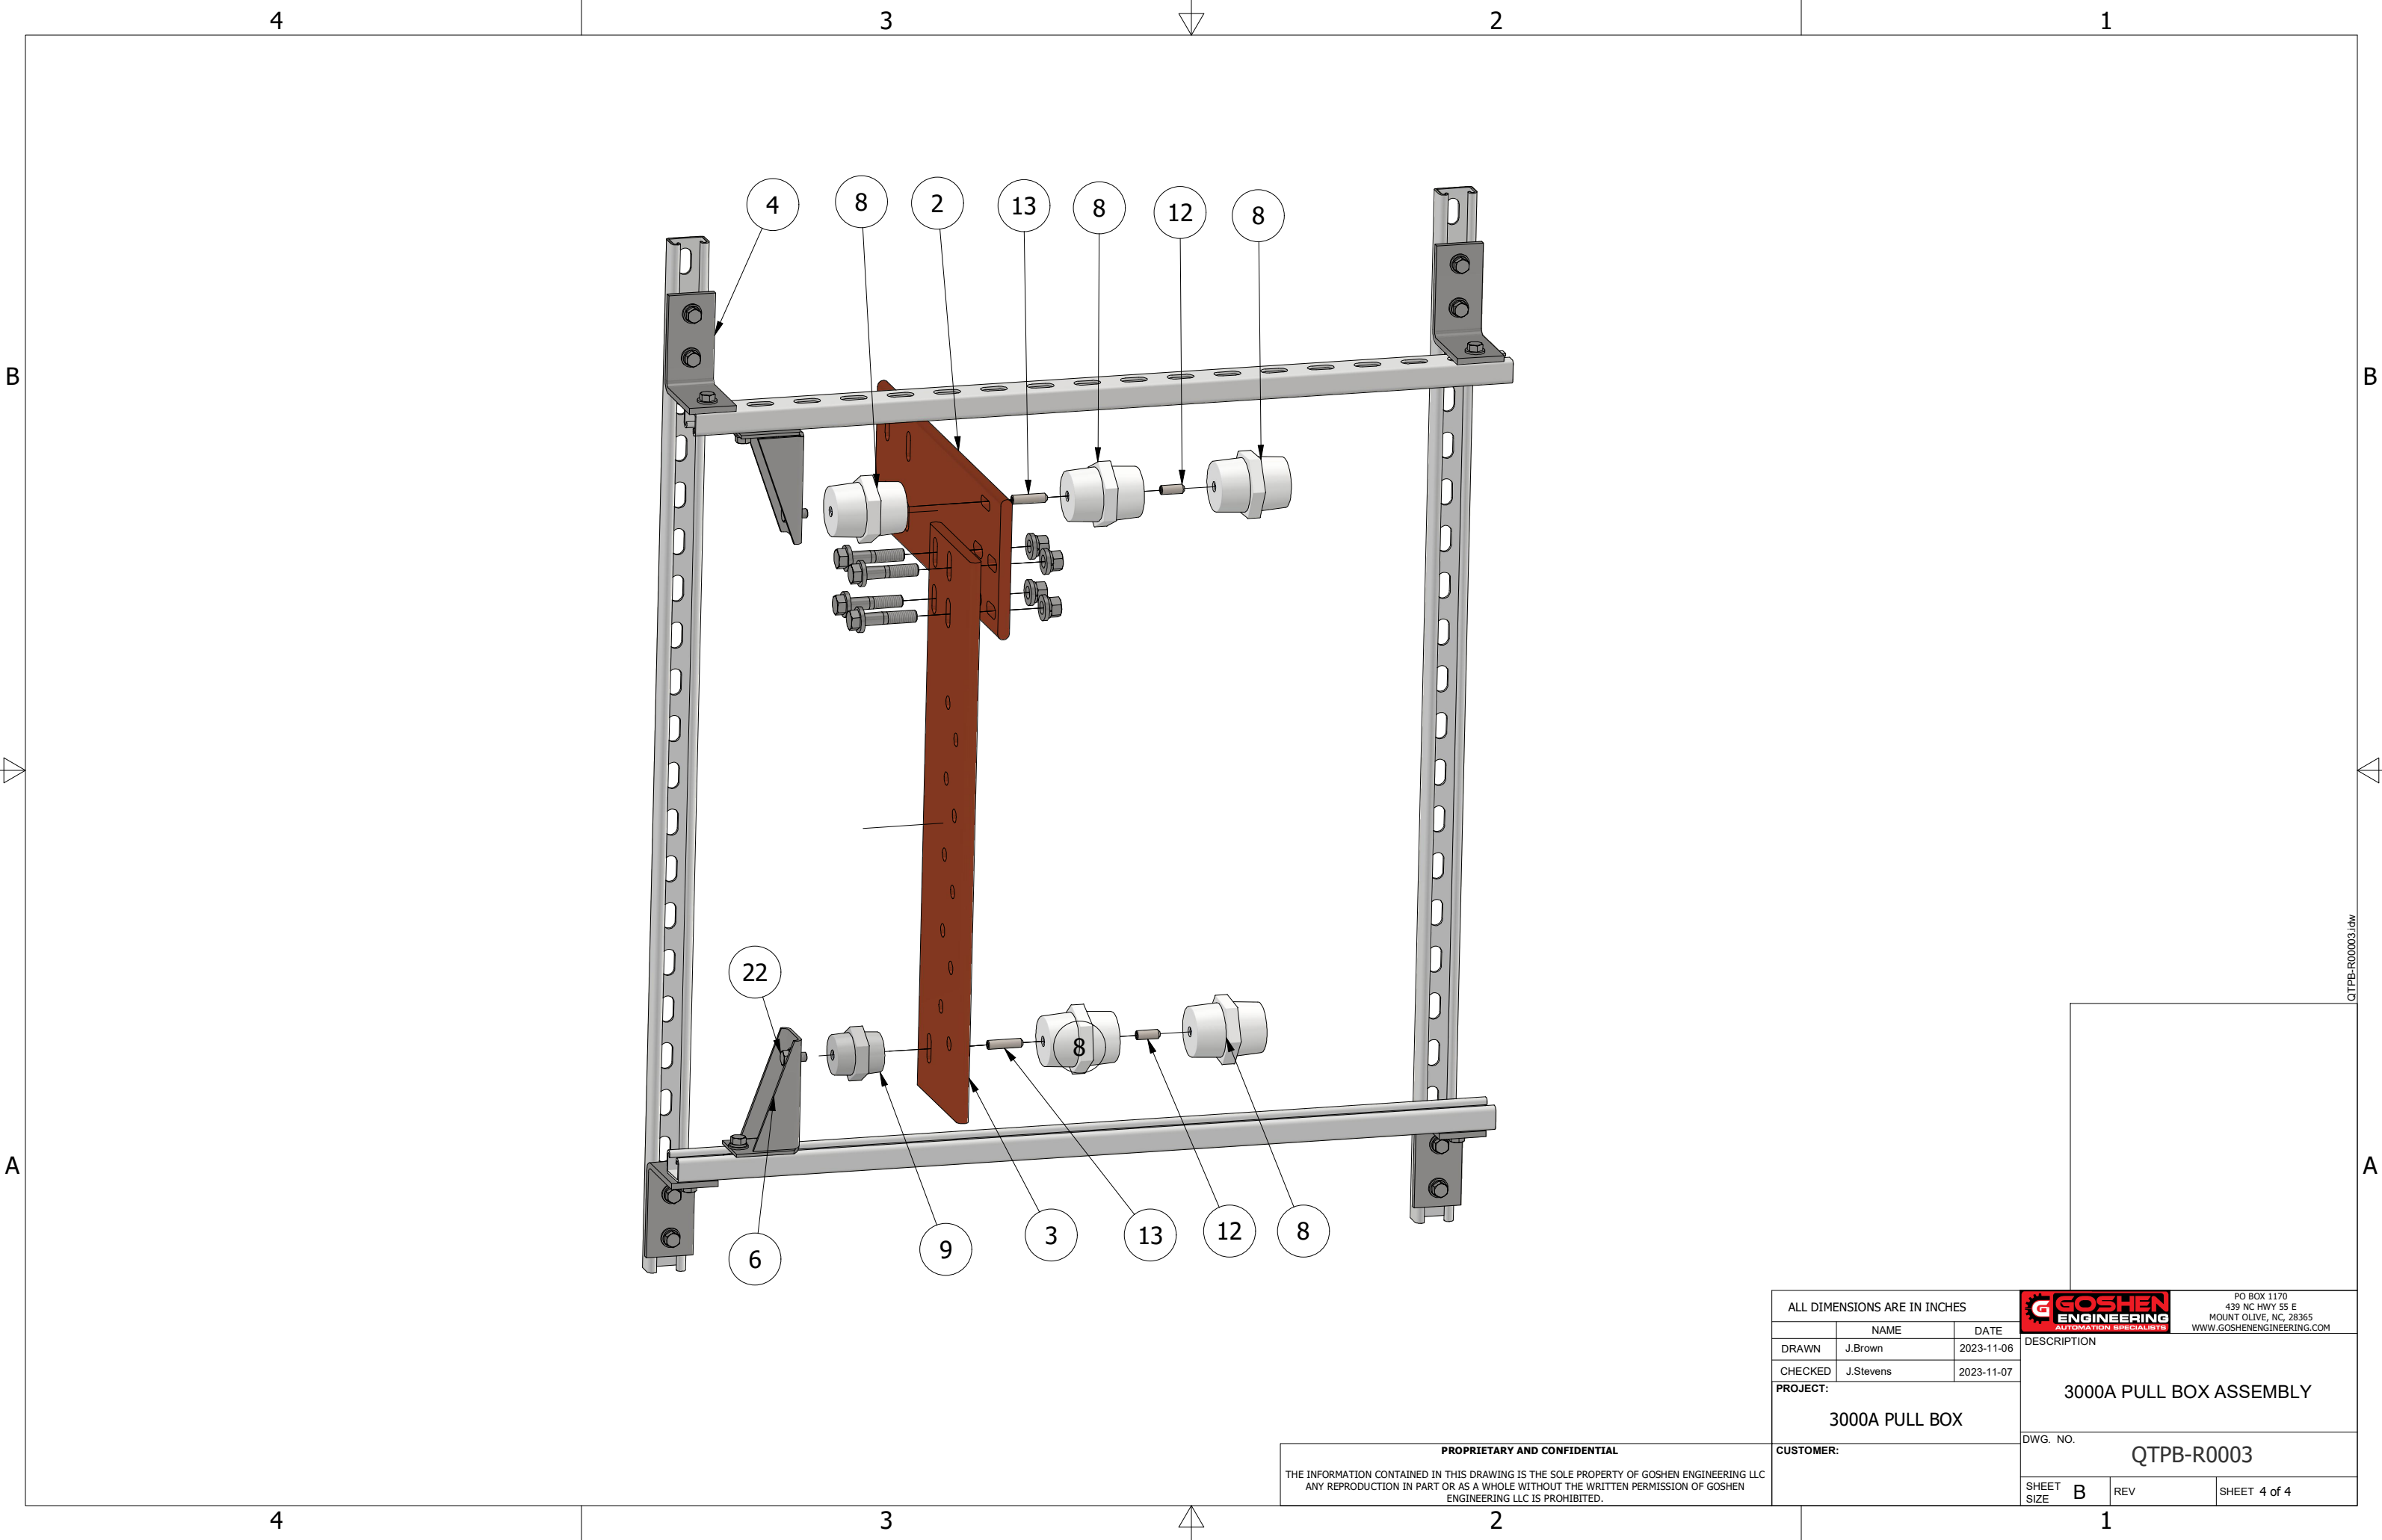

ALL DIMENSIONS ARE IN INCHES				PO BOX 1170 439 NC HWY 55 E MOUNT OLIVE, NC, 28365 WWW.GOSHENENGINEERING.COM		
	NAME	DATE		DESCRIPTION		
DRAWN	J.Brown	2023-11-06				
CHECKED	J.Stevens	2023-11-07				
PROJECT:						
3000A PULL BOX						
CUSTOMER:			DWG. NO.	QTPB-R0003		
			SHEET SIZE	B	REV	SHEET 4 of 4

PROPRIETARY AND CONFIDENTIAL
THE INFORMATION CONTAINED IN THIS DRAWING IS THE SOLE PROPERTY OF GOSHEN ENGINEERING LLC
ANY REPRODUCTION IN PART OR AS A WHOLE WITHOUT THE WRITTEN PERMISSION OF GOSHEN
ENGINEERING LLC IS PROHIBITED.